
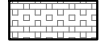
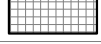


PROPOSED TILES BRAND-ROCELL



	SIZE	TILE CODE
	600 X 600 mm	RC.RSS.000112.SG.05 - SOLID SAND SEMI GLOSSY 600X600 mm
	300 X 600 mm	RC.001.000634.EM.0M- SOLID GRAY (MATT) 600X300mm
	600 X 600 mm	RP.OSC.007G2.MA.0M - SPECKLED GRAY (BRILLIANT MATT) 600X600mm
	600 X 600 mm	RC.002.000712.BM.05 - SPECKLED BROWN (BRILLIANT MATT) 600X600mm
	600 X 600 mm	RC.002.000708.BM.05 - SPECKLED GRAY (BRILLIANT MATT) 600X600mm (RAMP AREA WITH GROOVES AT 150mm C/C)
	600 X 600 mm	RC.RSS.000713.MA.05 - SPECKLED DARK GRAY 600X600mm
	300 X 300 mm	50 mm CONCRETE PAVING TILE
	600 X 600 mm	THRESHOLD TILE RC.RSS.000713.MA.05 - SPECKLED DARK GRAY 600X600mm
	600 X 300 mm	RP.MOC.0001PW.GL.0M - SOLID IVORY 600X300 mm (GLOSSY) FOR TOILET WALL TILED HEIGHT- REFER TOILET DETAIL DRAWINGS

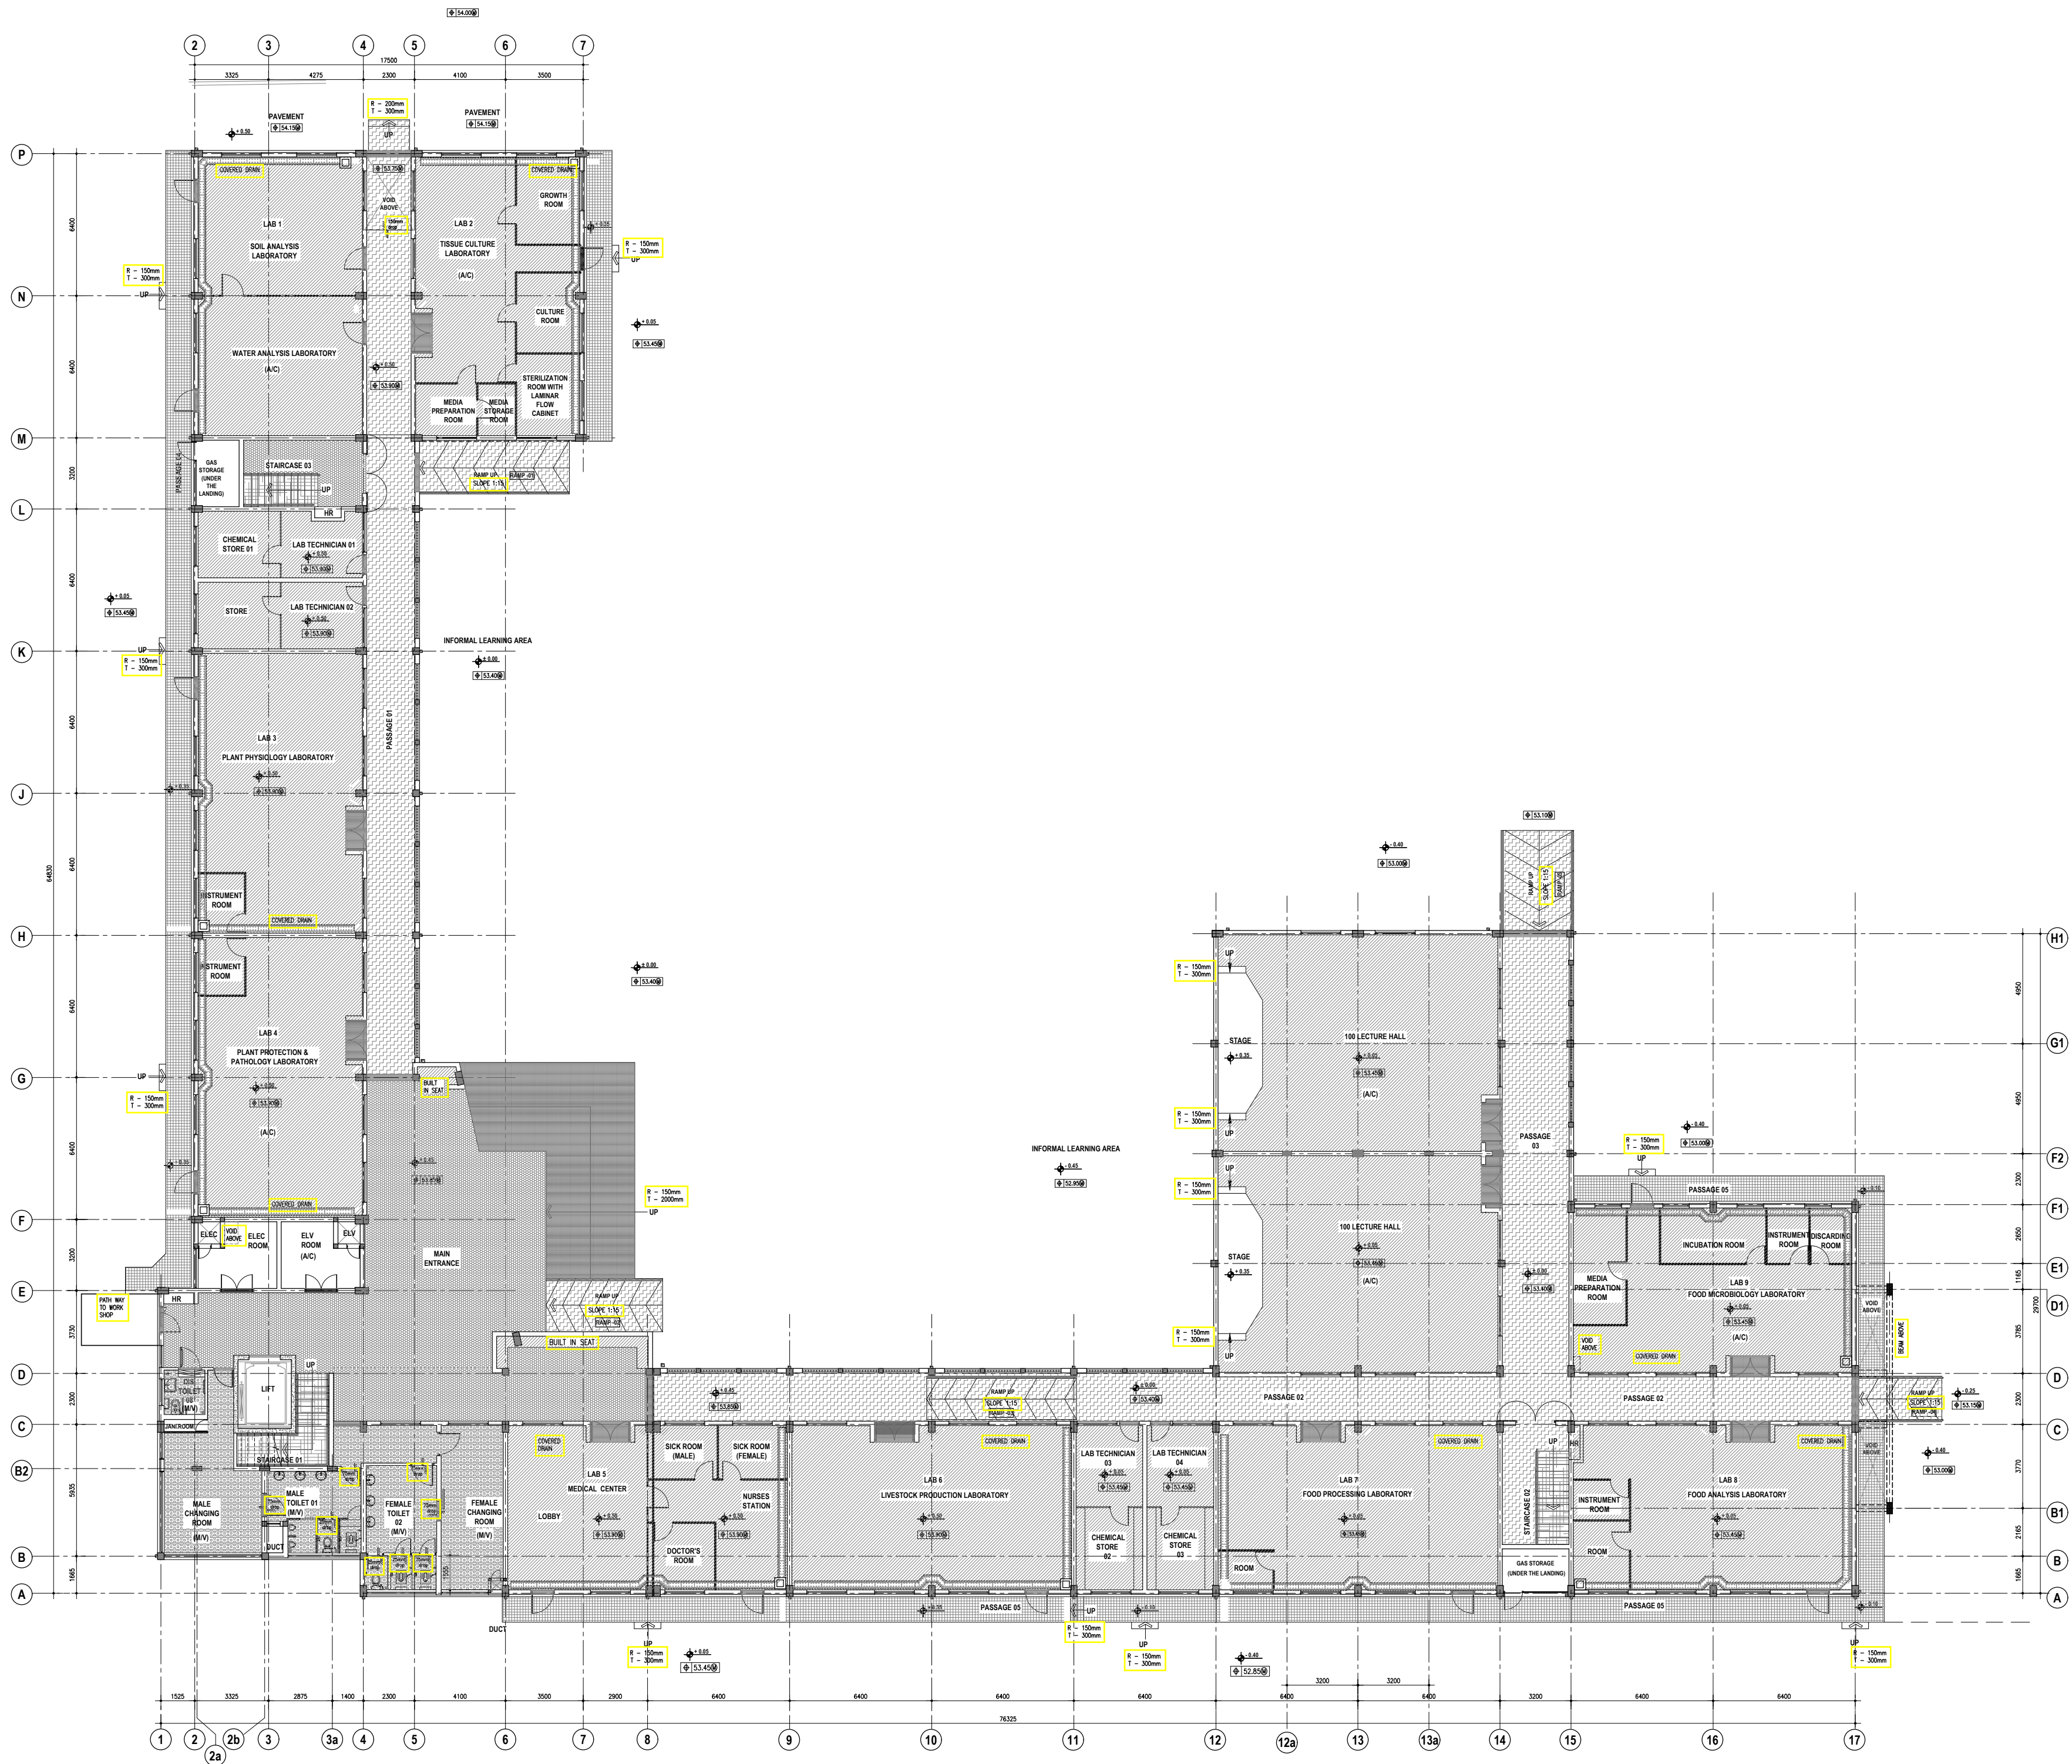


GROUND FLOOR

SCALE-1:200



PROPOSED TILES BRAND-ROCELL

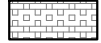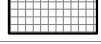	SIZE	TILE CODE
	600 X 600 mm	RC.RSS.000112.SG.05 - SOLID SAND SEMI GLOSSY 600X600 mm
	300 X 600 mm	RC.001.000634.EM.0M- SOLID GRAY (MATT) 600X300mm
	600 X 600 mm	RP.OSC.007G2.MA.0M- SPECKLED GRAY (BRILLIANT MATT) 600X600mm
	600 X 600 mm	RC.002.000712.BM.05 - SPECKLED BROWN (BRILLIANT MATT) 600X600mm
	600 X 600 mm	RC.002.000708.BM.05 - SPECKLED GRAY (BRILLIANT MATT) 600X600mm (RAMP AREA WITH GROOVES AT 150mm C/C)
	600 X 600 mm	RC.RSS.000713.MA.05 - SPECKLED DARK GRAY 600X600mm
	300 X 300 mm	50 mm CONCRETE PAVING TILE
	600 X 600 mm	THRESHOLD TILE RC.RSS.000713.MA.05 - SPECKLED DARK GRAY 600X600mm
	600 X 300 mm	RP.MOC.0001PW.GL.0M - SOLID IVORY 600X300 mm (GLOSSY) FOR TOILET WALL TILED HEIGHT- REFER TOILET DETAIL DRAWINGS

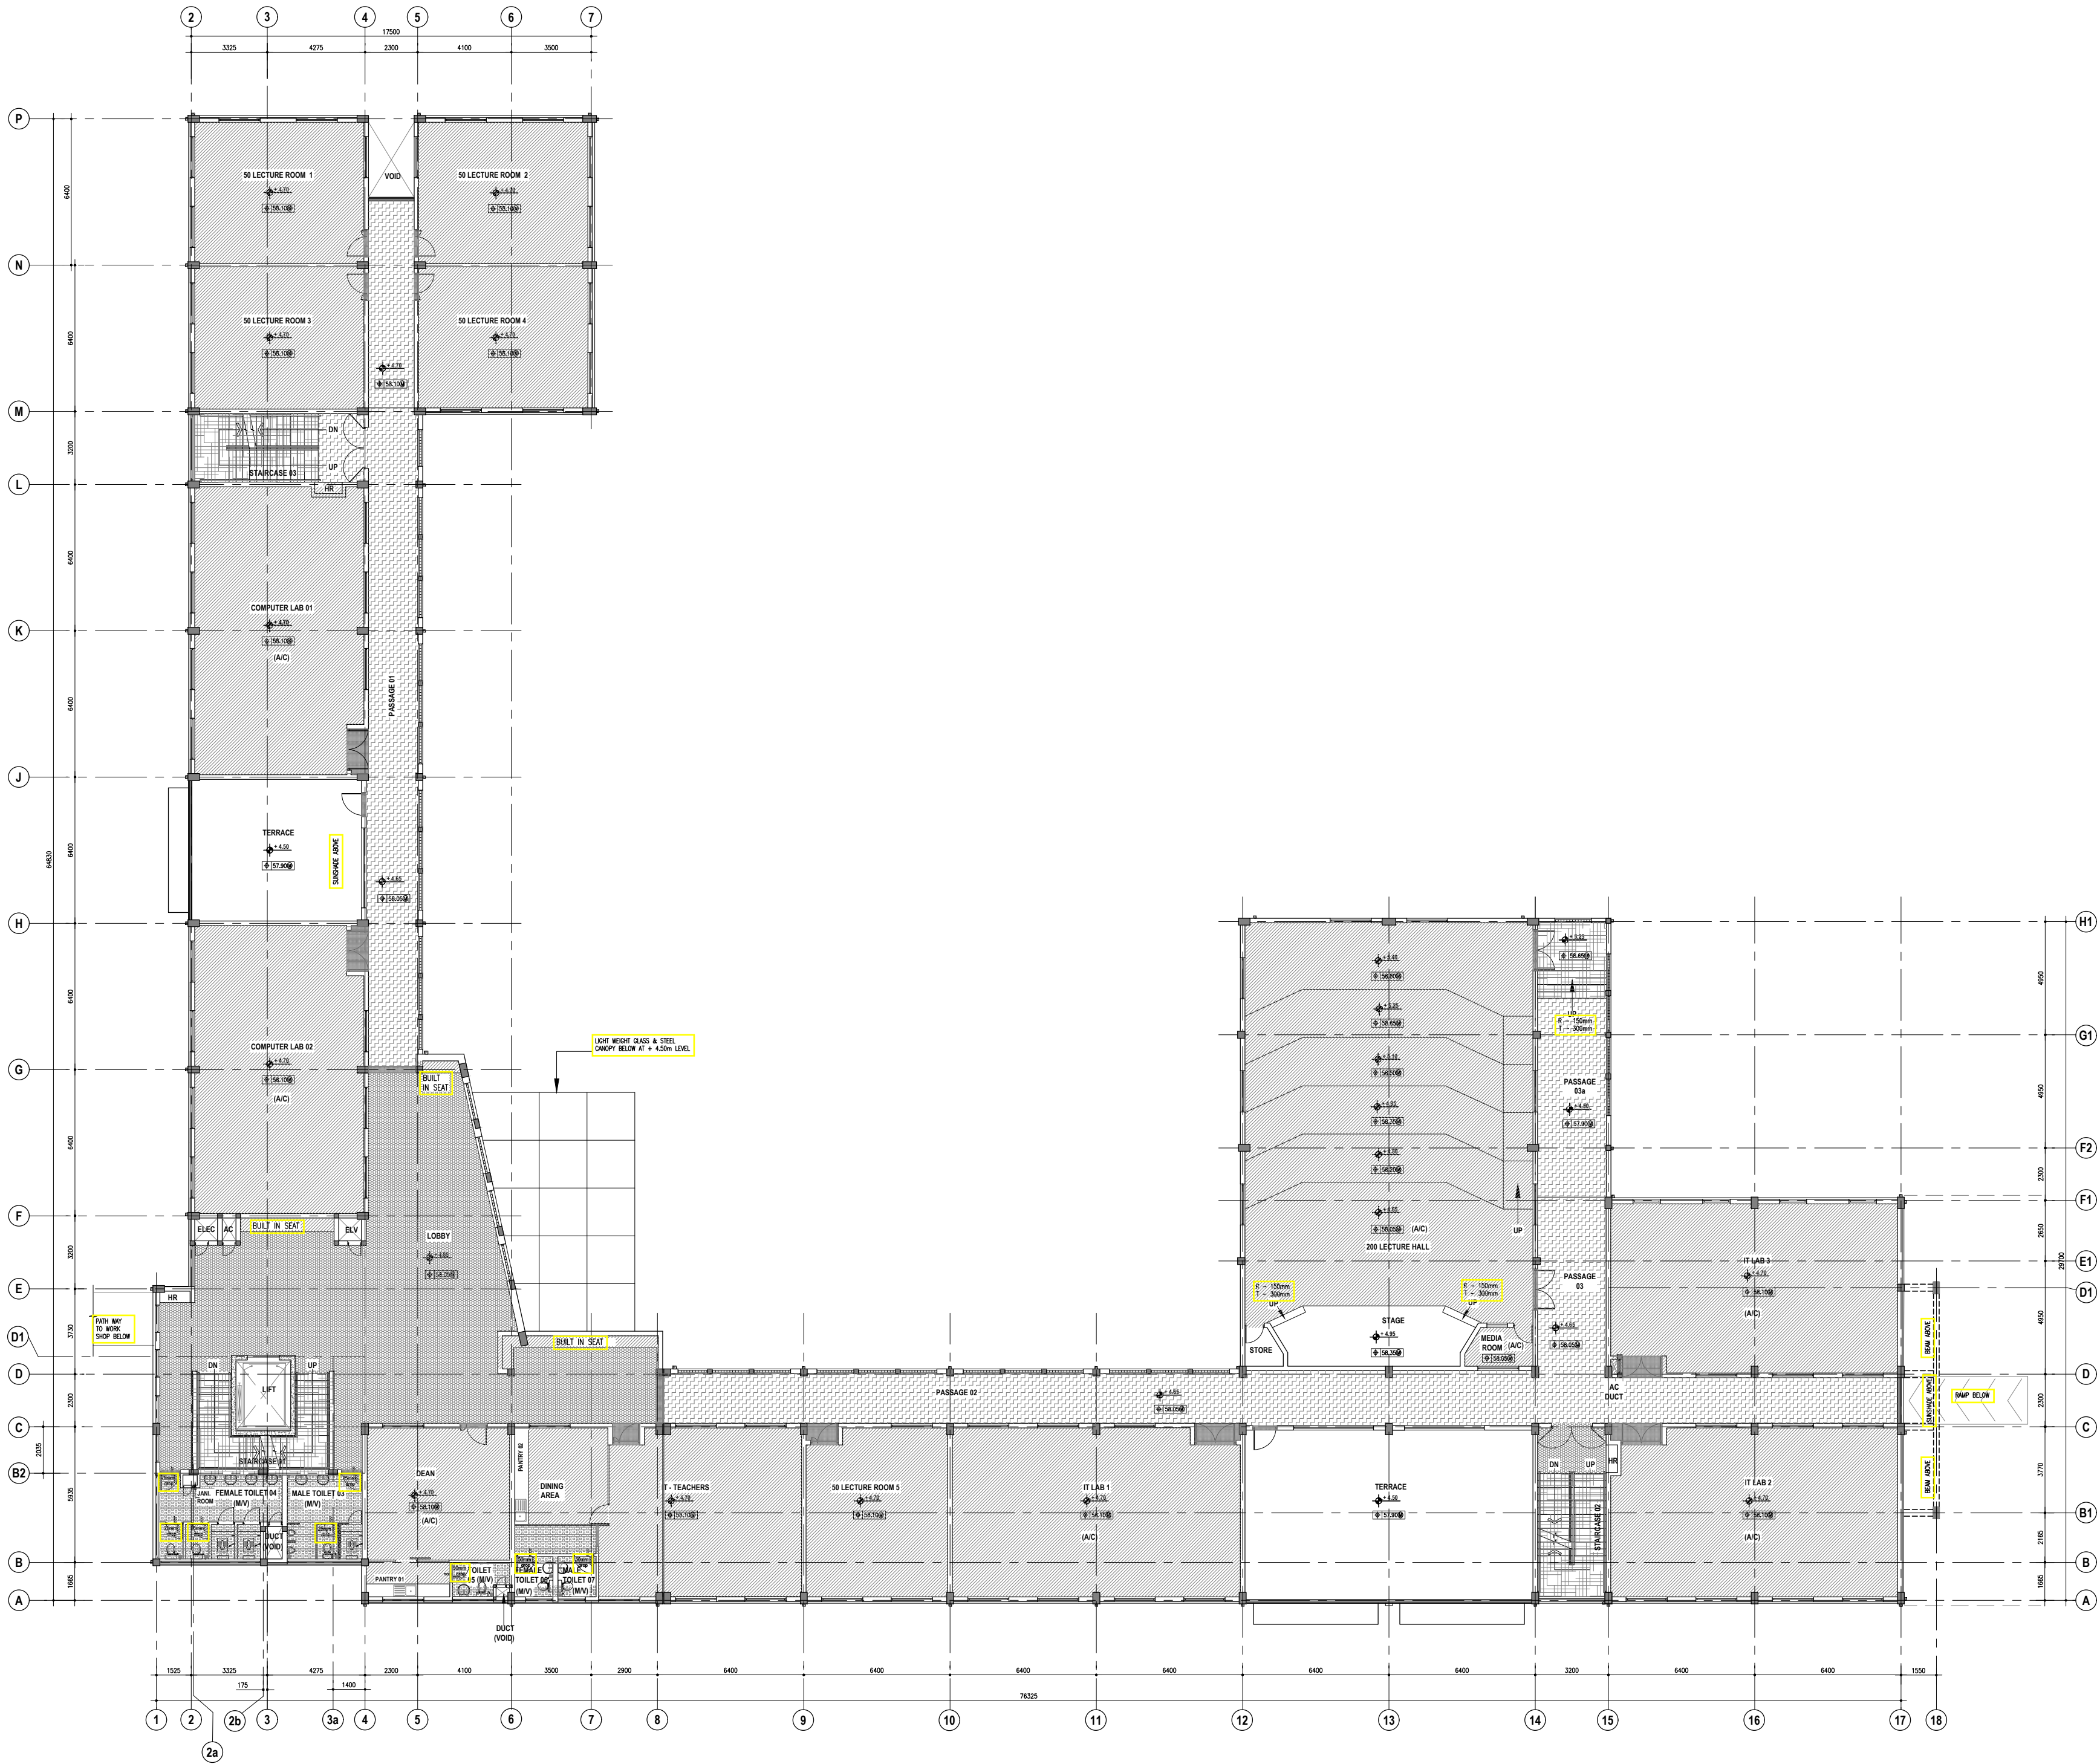

FIRST FLOOR
SCALE-1:200

PROPOSED TILES BRAND-ROCELL

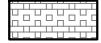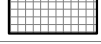	SIZE	TILE CODE
	600 X 600 mm	RC.RSS.000112.SG.05 - SOLID SAND SEMI GLOSSY 600X600 mm
	300 X 600 mm	RC.001.000634.EM.0M- SOLID GRAY (MATT) 600X300mm
	600 X 600 mm	RP.OSC.007G2.MA.0M- SPECKLED GRAY (BRILLIANT MATT) 600X600mm
	600 X 600 mm	RC.002.000712.BM.05 - SPECKLED BROWN (BRILLIANT MATT) 600X600mm
	600 X 600 mm	RC.002.000708.BM.05 - SPECKLED GRAY (BRILLIANT MATT) 600X600mm (RAMP AREA WITH GROOVES AT 150mm C/C)
	600 X 600 mm	RC.RSS.000713.MA.05 - SPECKLED DARK GRAY 600X600mm
	300 X 300 mm	50 mm CONCRETE PAVING TILE
	600 X 600 mm	THRESHOLD TILE RC.RSS.000713.MA.05 - SPECKLED DARK GRAY 600X600mm
	600 X 300 mm	RP.MOC.0001PW.GL.0M - SOLID IVORY 600X300 mm (GLOSSY) FOR TOILET WALL TILED HEIGHT- REFER TOILET DETAIL DRAWINGS




SECOND FLOOR
SCALE-1:200


	SIZE	TILE CODE
	600 X 600 mm	RC.RSS.000112.SG.05 - SOLID SAND SEMI GLOSSY 600X600 mm
	300 X 600 mm	RC.001.000634.EM.0M- SOLID GRAY (MATT) 600X300mm
	600 X 600 mm	RP.OSC.007G2.MA.0M- SPECKLED GRAY (BRILLIANT MATT) 600X600mm
	600 X 600 mm	RC.002.000712.BM.05 - SPECKLED BROWN (BRILLIANT MATT) 600X600mm
	600 X 600 mm	RC.002.000708.BM.05 - SPECKLED GRAY (BRILLIANT MATT) 600X600mm (RAMP AREA WITH GROOVES AT 150mm C/C)
	600 X 600 mm	RC.RSS.000713.MA.05 - SPECKLED DARK GRAY 600X600mm
	300 X 300 mm	50 mm CONCRETE PAVING TILE
	600 X 600 mm	THRESHOLD TILE RC.RSS.000713.MA.05 - SPECKLED DARK GRAY 600X600mm
	600 X 300 mm	RP.MOC.0001PW.GL.0M - SOLID IVORY 600X300 mm (GLOSSY) FOR TOILET WALL TILED HEIGHT- REFER TOILET DETAIL DRAWINGS



SCALE-1:200

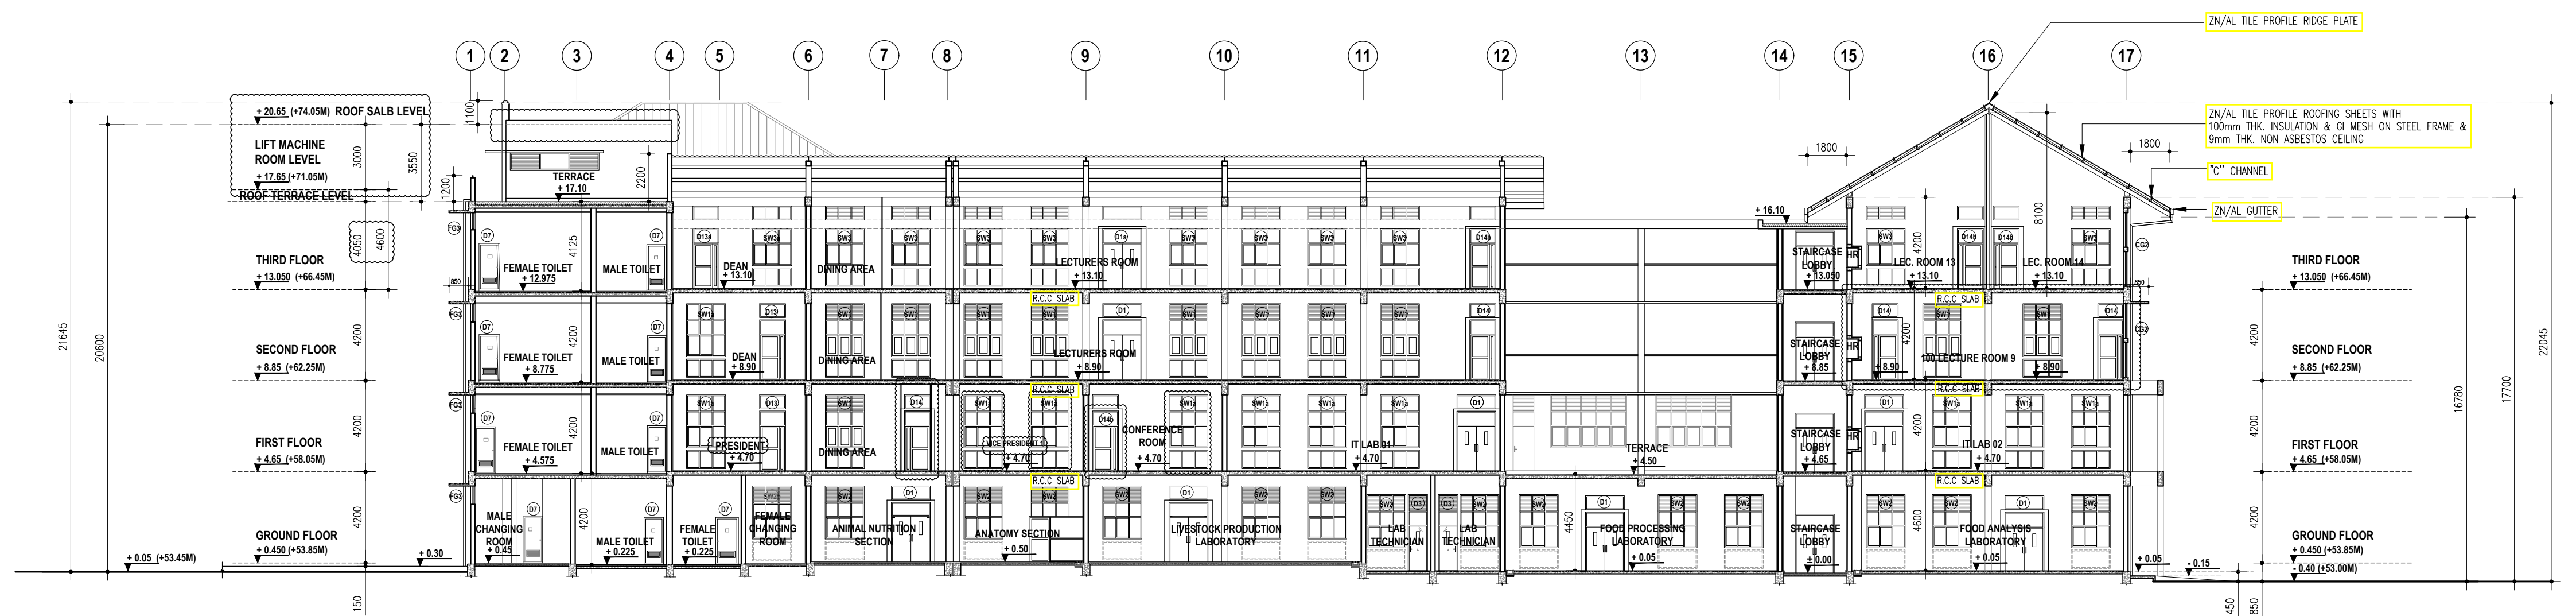


SECTION A-A

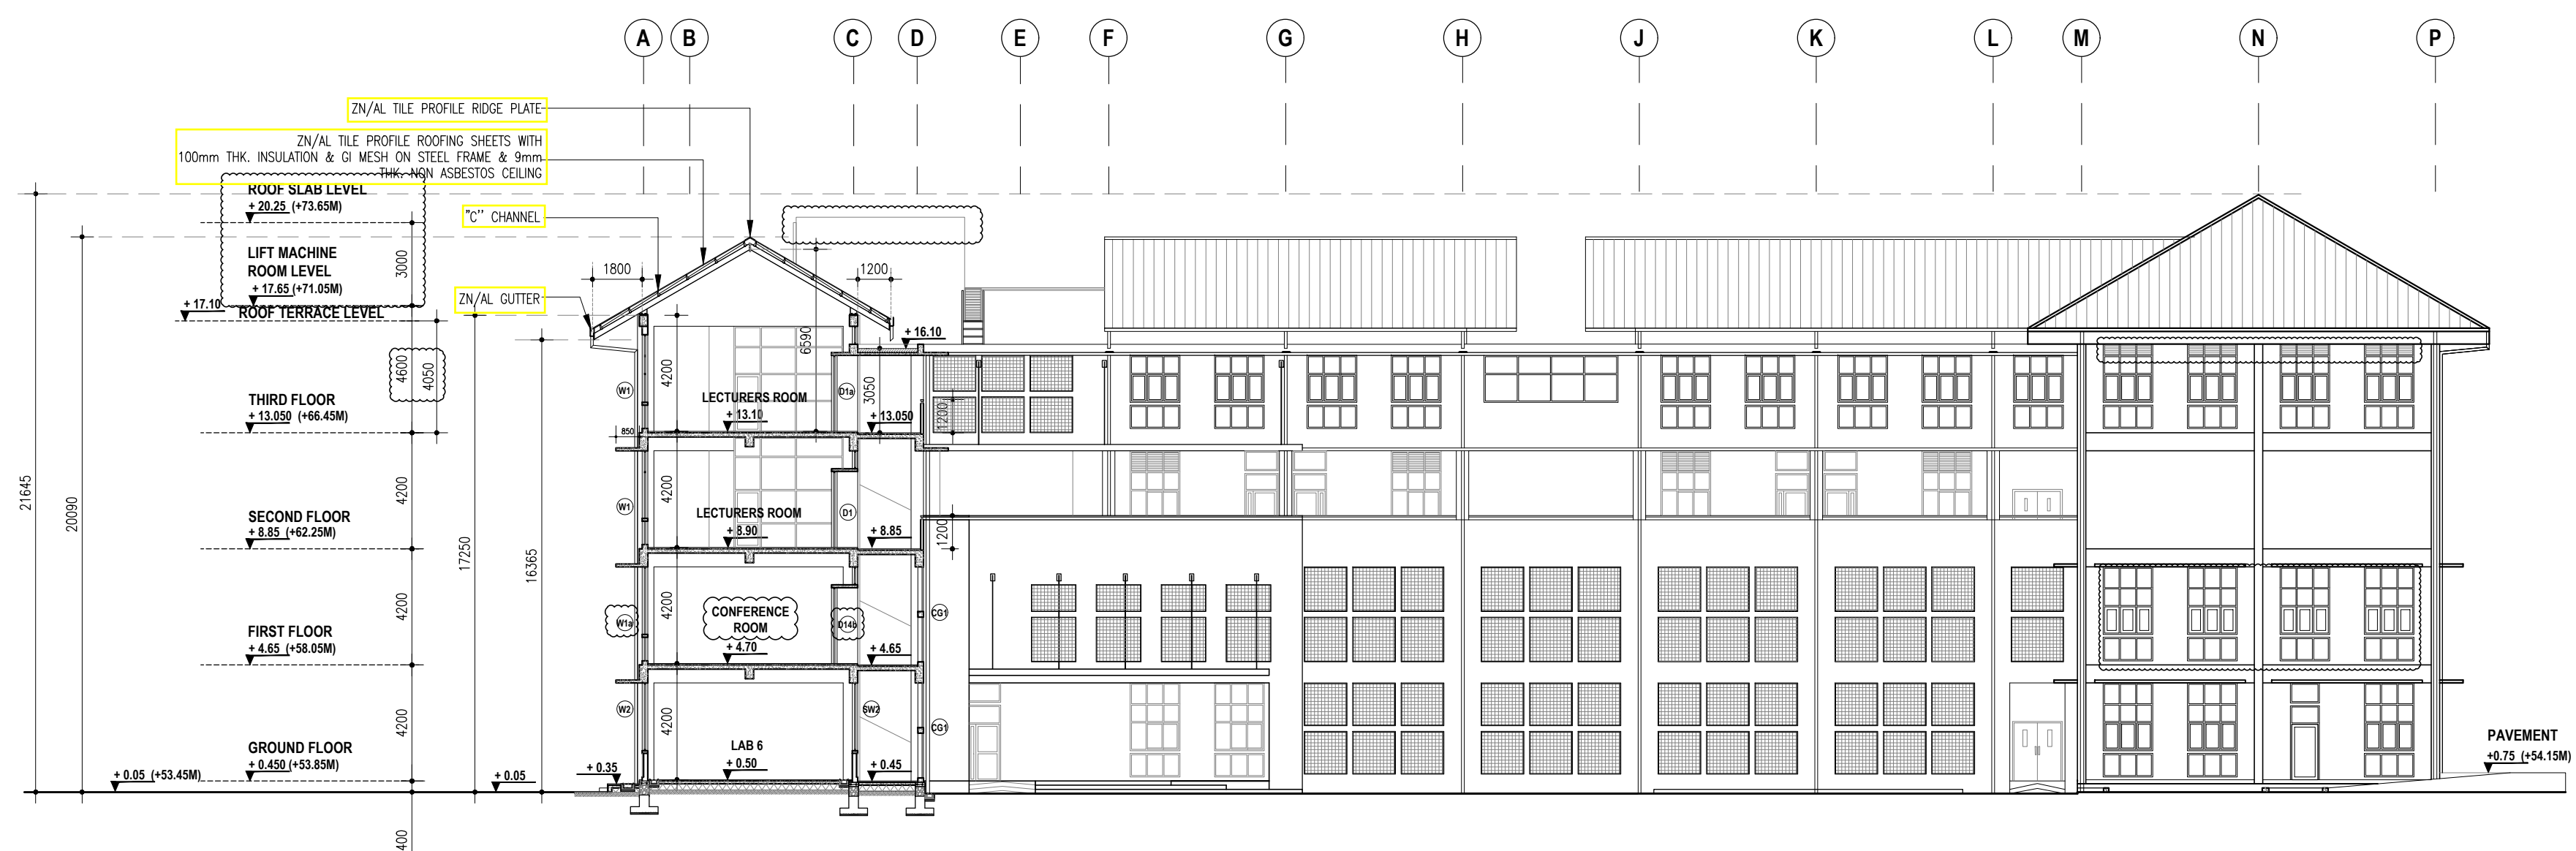


SECTION B-B



ELEVATION A

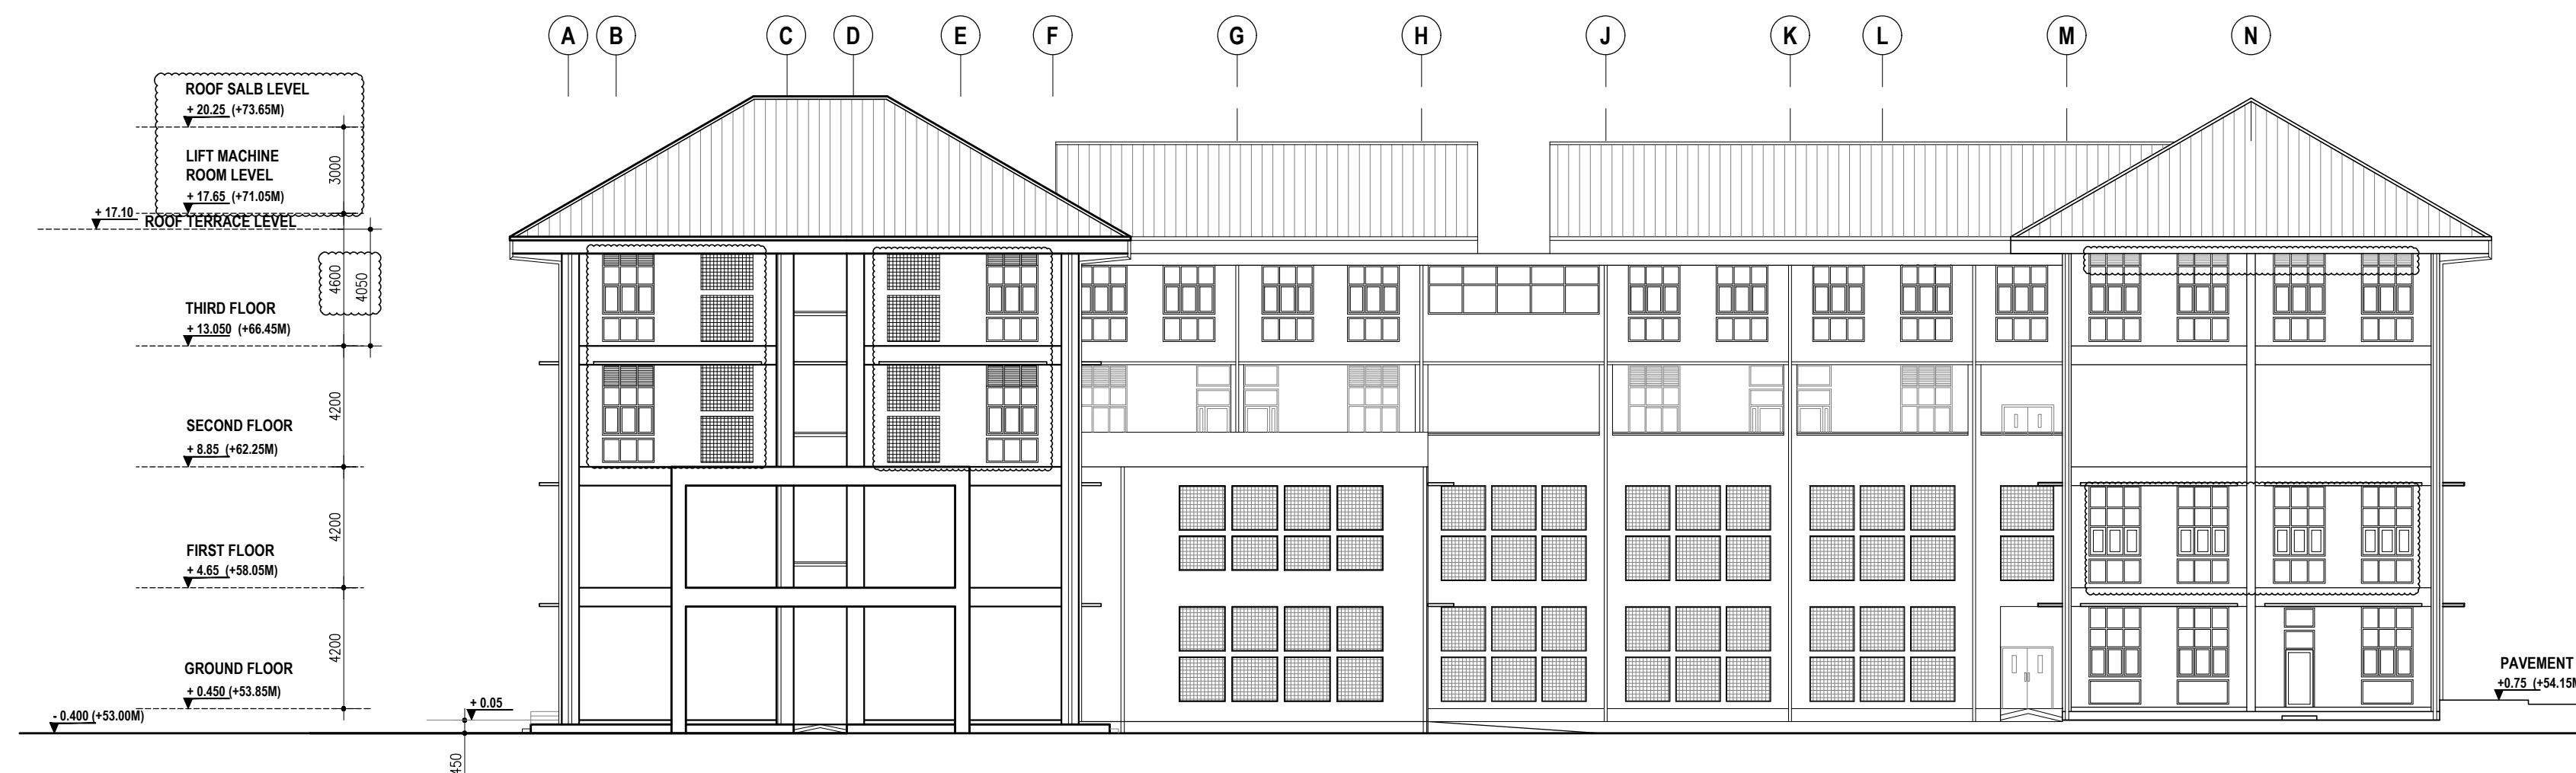

ELEVATION B

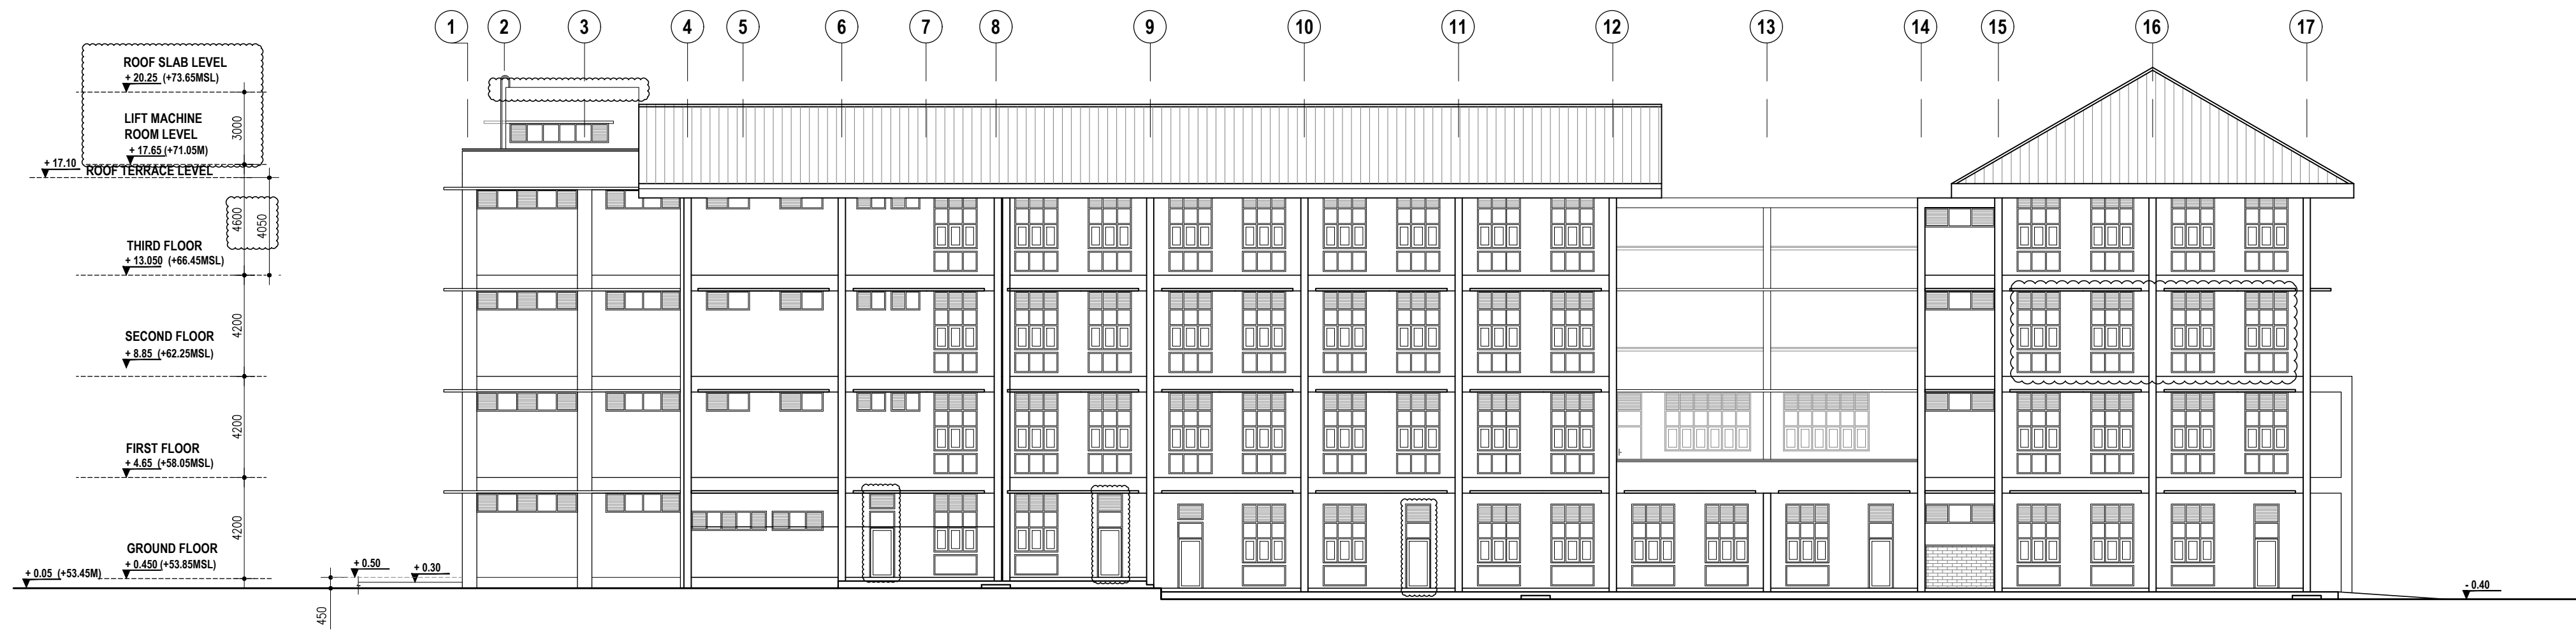

ELEVATION C



ELEVATION D